


HINWEIS:
FLÄCHEN- UND MASZANGABEN GEMÄSZ DER ZUR VERFÜGUNG GESTELLTEN
BESTANDSUNTERLAGEN DES AUFTRAGGEBERS.

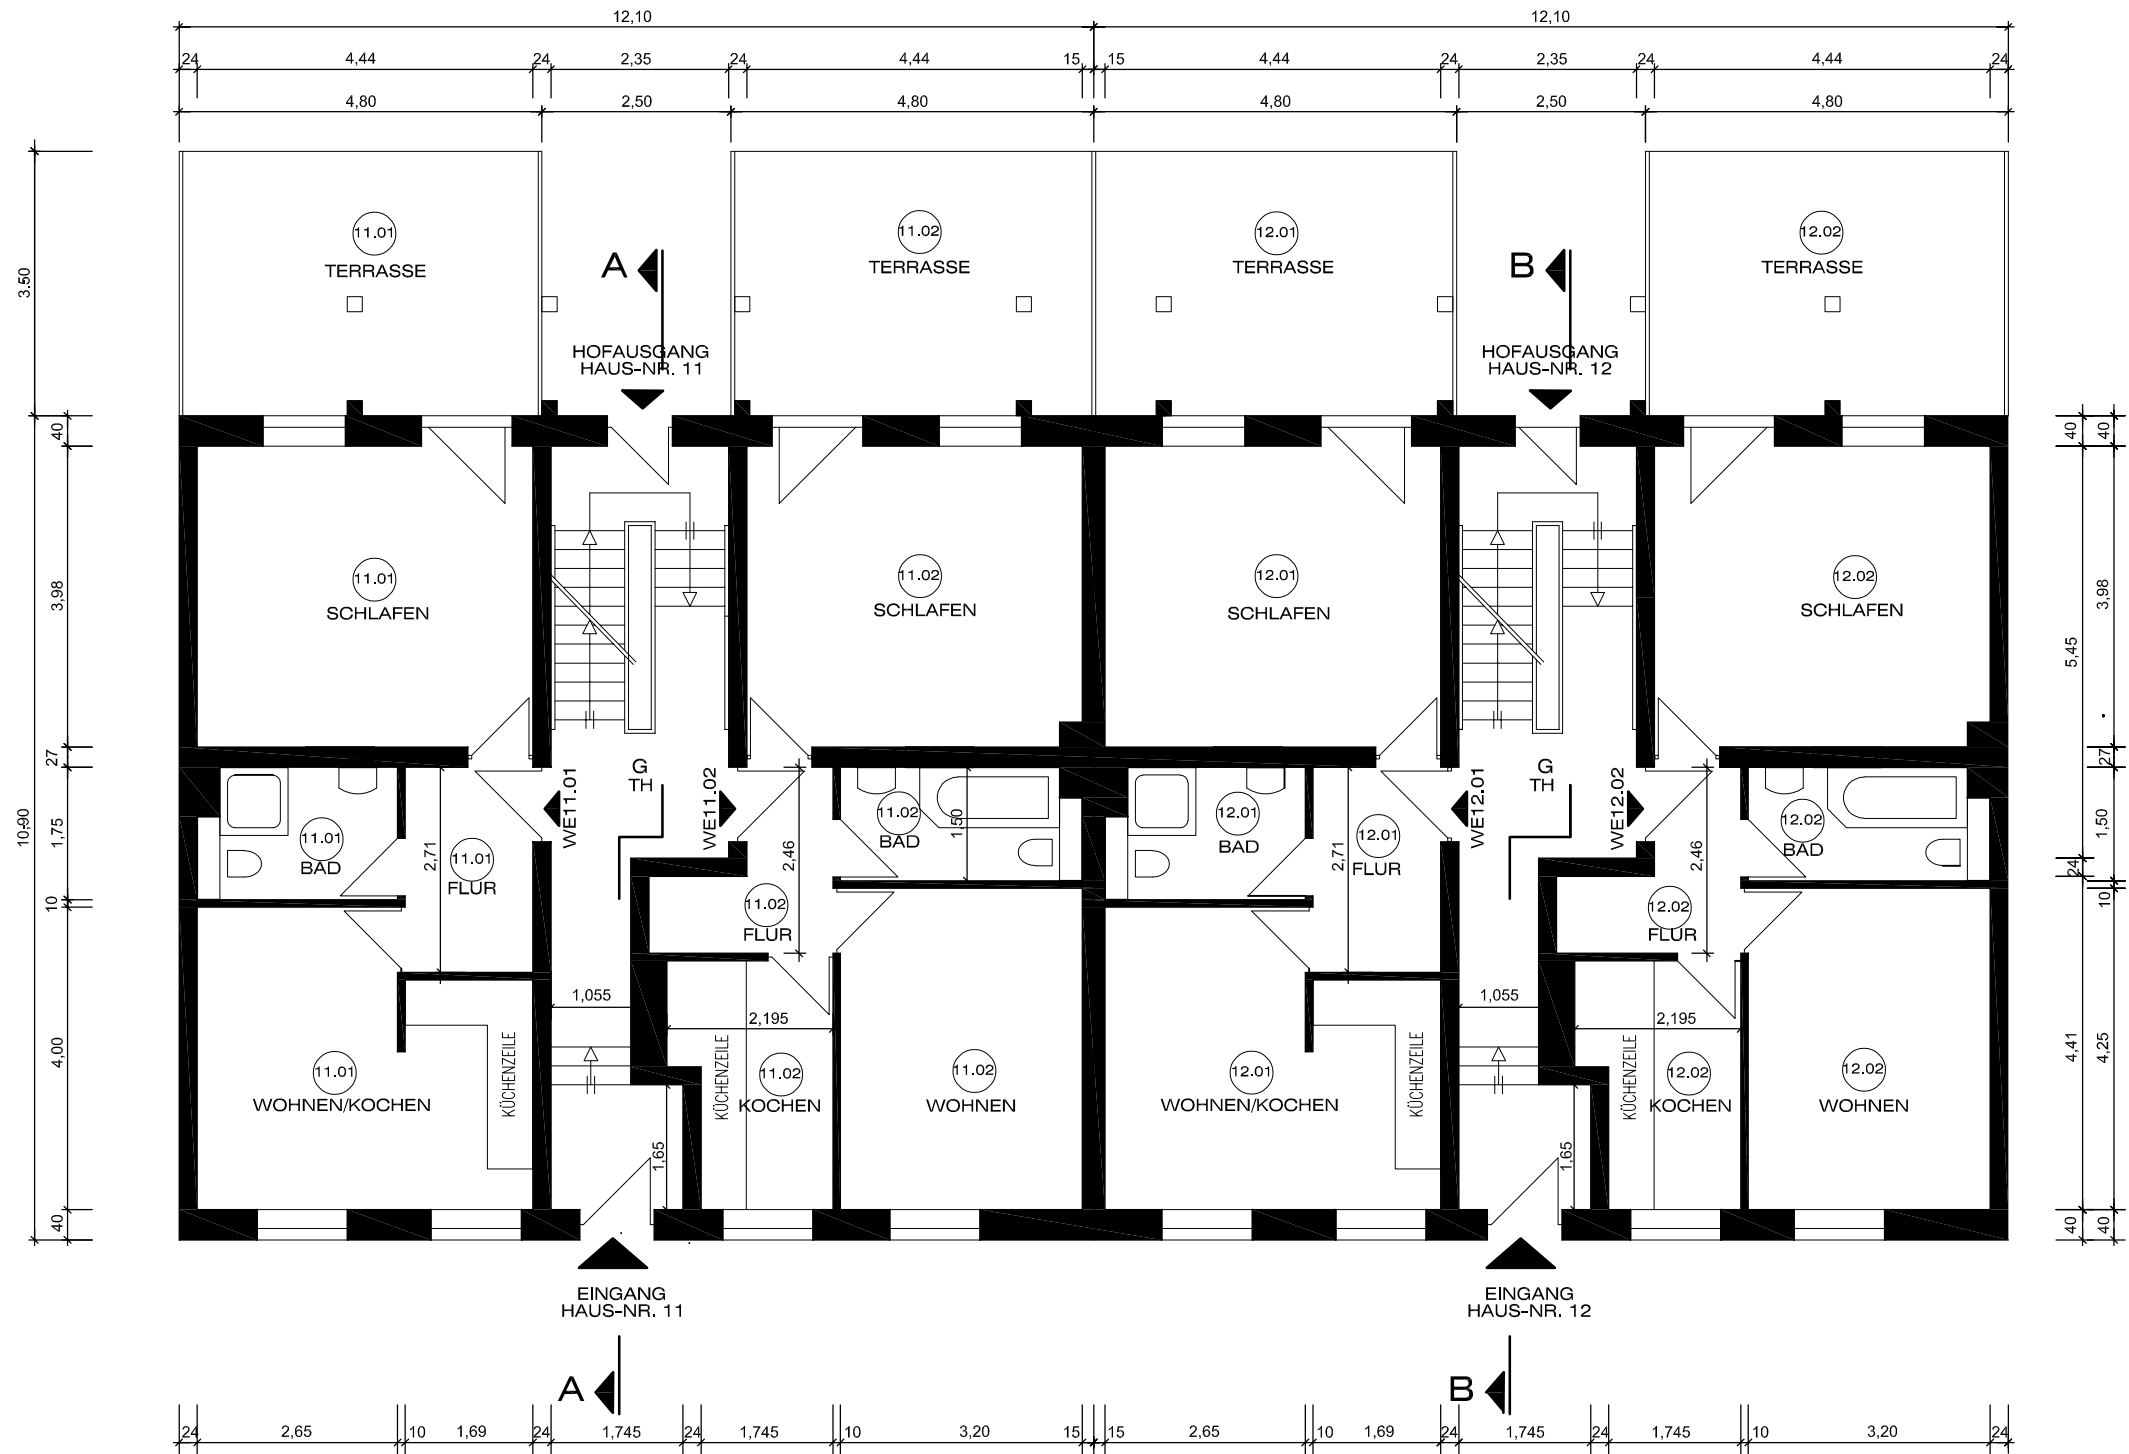

WE 11.01 / 2-RAUM-WE		
(11.01)	WOHNEN/KOCHEN	15,95m ²
(11.01)	SCHLAFEN	17,97m ²
(11.01)	BAD	4,11m ²
(11.01)	FLUR	4,58m ²
(11.01)	TERRASSE (ZUR HÄLFTE)	8,22m ²
GESAMTWOHNFLÄCHE WE 11.01		50,83m ²

WE 11.02 / 2-RAUM-WE		
(11.02)	WOHNEN	13,60m ²
(11.02)	KOCHEN	6,37m ²
(11.02)	SCHLAFEN	17,87m ²
(11.02)	BAD	4,35m ²
(11.02)	FLUR	4,12m ²
(11.02)	TERRASSE (ZUR HÄLFTE)	8,22m ²
GESAMTWOHNFLÄCHE WE 11.02		54,53m ²

WE 12.01 / 2-RAUM-WE		
(12.01)	WOHNEN/KOCHEN	15,95m ²
(12.01)	SCHLAFEN	17,97m ²
(12.01)	BAD	4,11m ²
(12.01)	FLUR	4,58m ²
(12.01)	TERRASSE (ZUR HÄLFTE)	8,22m ²
GESAMTWOHNFLÄCHE WE 12.01		50,83m ²

WE 12.02 / 2-RAUM-WE		
(12.02)	WOHNEN	13,60m ²
(12.02)	KOCHEN	6,37m ²
(12.02)	SCHLAFEN	17,87m ²
(12.02)	BAD	4,35m ²
(12.02)	FLUR	4,12m ²
(12.02)	TERRASSE (ZUR HÄLFTE)	8,22m ²
GESAMTWOHNFLÄCHE WE 12.02		54,53m ²

G GEMEINSCHAFTSEIGENTUM

STAND 06.11.2025

BAUHERR
SANDAY GmbH
VERTR. DURCH: ROBERT HÖHNE
BERGSTRASSE 4
16356 AHRENSFELDE

PLANVERFASSTER
planungsbüro möller
dipl.-ing. michael möller
MÜHLENSTRASSE 9, 18055 ROSTOCK
TEL 0381/ 4 90 96 97 / info@pb-moeller.de

VORHABEN
MEHRFAMILIENHAUS
GELLERTSTRASSE 11-12
18057 ROSTOCK

ANTRAG AUF ABGESCHLOSSENHEIT

DATUM	BEARB.	GEPR.	FREIGABE
31.07.2025	U. KLEIST		M. MÖLLER

PLANBEZEICHNUNG
AUFTEILUNGSPLAN 1:100
GRUNDRISS EG

PLAN-NR.

A 1.1

GRUNDRISS EG

DATUM/UNTERSCHRIFT ANTRAGSTELLER/BAUHERR

